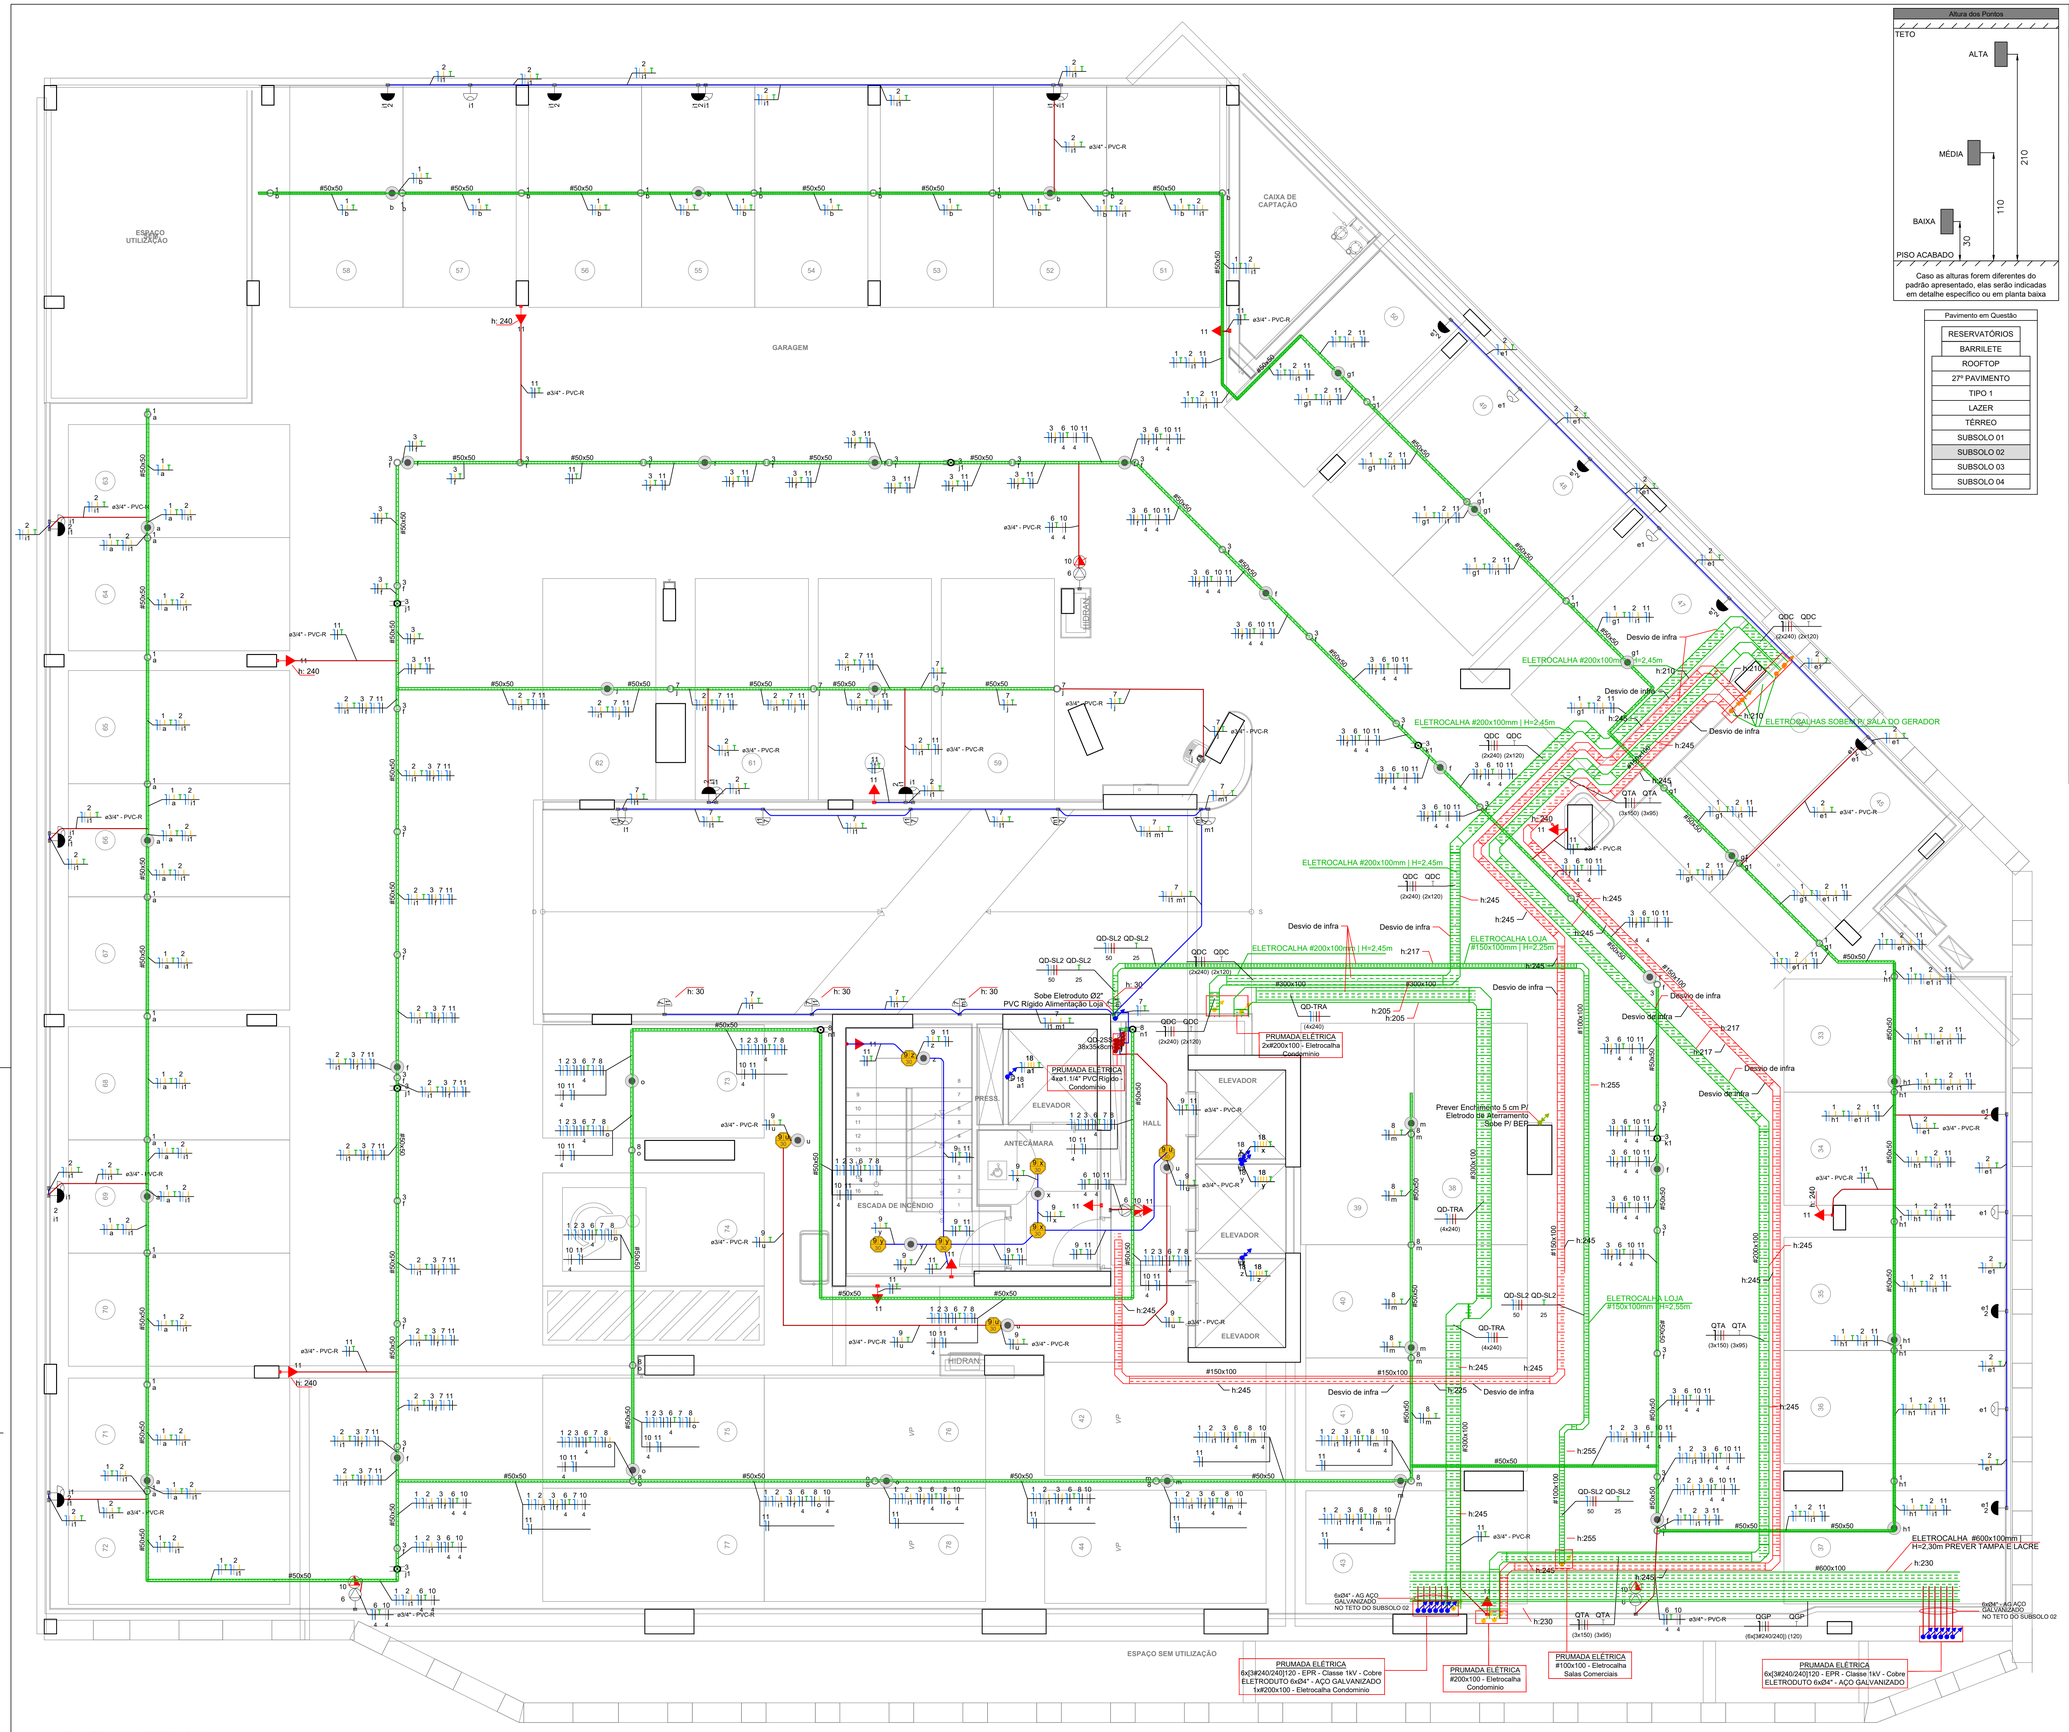

PLANTA BAIXA SUBSOLO 02

1:50

Altura dos Pontos	
TETO	
ALTA	
MÉDIA	210
BAIXA	110
PISO ACABADO	30

Caso as alturas forem diferentes do padrão apresentado, elas serão indicadas em detalhe específico ou em planta baixa

Pavimento em Questão
RESERVATÓRIOS
BARRILETE
ROOFTOP
27º PAVIMENTO
TIPO 1
LAZER
TÉRREO
SUBSOLO 01
SUBSOLO 02
SUBSOLO 03
SUBSOLO 04

Legenda - 2SS
Curva horizontal 45°
Curva horizontal 90°
Curva vertical interna 45°
Luminária Tartaruga - 30 W
Luminária de parede, instalação à 210cm do piso acabado.
Luminária de parede, instalação à 30cm do piso acabado.
Luminária grande - 30W - Laje
Luminária pequena - 10W - Teto
Ponto para Sensor de Presença - Teto
Ponto para alimentação de fita de LED.
Quadro de Distribuição Elétrica - Embutido - PVC - Tigre - H=150cm
Sensor de Presença - Teto
Sensor de Presença de Parede - Alta
Tomada 10A Simples - Alta - Bloco Autônomo
Tomada 10A Simples em Conduiete - Alta - Preventivo
Tomada 20A Simples (220V) - Média
Tomada 20A Simples - Baixa

LEGENDA	
	Elétrica - Eletroduto PVC Antichama embutido - ø3/4"
	Elétrica - Eletroduto PVC Antichama embutido no piso - ø3/4"
	Elétrica - Eletroduto PEAD Antichama enterrado - ø3/4"
	Elétrica - Eletroduto PVC Antichama aparente - ø3/4"
PVC-R	Elétrica - Eletroduto PVC Rígido Antichama aparente - ø3/4"
AG	Elétrica - Eletroduto Aço Galvanizado aparente - ø3/4"
	Malha de Aterramento - Eletroduto / cabo cobre NU
	Telemedição - Eletroduto PVC Antichama embutido - ø1"
	Telemedição - Eletroduto PVC Antichama embutido - ø1"
	Automação - Eletroduto PVC Antichama embutido - ø3/4"
	Automação - Eletroduto PVC Antichama embutido no piso - ø3/4"
	Automação Sinal - Eletroduto PVC Antichama embutido - ø3/4"
	Automação Sinal - Eletroduto PVC Antichama embutido no piso - ø3/4"
	Perfilado tipo C, ferro galvanizado eletrolítico
	Eletrocalha Lisa tipo U, ferro galvanizado eletrolítico
	Eletrocalha Perfurada tipo U, ferro galvanizado eletrolítico
	Barramento Blindado

NOTAS

1) Eletrodutos não especificados terão ø3/4" e serão de PVC - Antichama.
2) Condutores não especificados terão #2.5mm² e terão isolamento para 750V - Antichama.
3) O memorial descritivo é parte integrante do projeto elétrico e suas orientações deverão ser rigorosamente seguidas.
4) Os condutores deverão ter as seguintes cores:
- Fase R - cor preta
- Fase S - cor branco
- Fase T - cor vermelha
- Neutro - cor azul claro
- Retorno - cor amarelo
- Proteção - cor verde ou verde-amarelo
5) Fica facultativo o uso da fiação de retorno com #1,5 mm².
6) Aplicação dos eletrodutos flexíveis (NBR 15465)
a) embutido em laje: médio ou pesado (conforme legenda)
b) embutido em alvenaria ou aparente no teto: leve (conforme legenda)
c) enterrado: PEAD
7) Toda travessia de piso deve ser obturada de modo a impedir a propagação de incêndio.
8) As canalizações de gás devem estar a um afastamento mínimo de 0,30m das tubulações de outra natureza, em especial eletrodutos e pontos elétricos.
9) Nas salas comerciais, interligar o quadro de distribuição telecom com o quadro de distribuição elétrico com duas tubulações de ø3/4".
10) A proteção contra sobrecargas dos circuitos dos motores utilizados nos serviços de SCI (bombas de incêndio, sistemas de extração de fumaça, etc) não é permitida.
11) É admitido o uso de disjuntor com proteção somente magnética, sendo que, neste caso, o responsável técnico deverá comprovar essa exigência mediante apresentação da ficha técnica do dispositivo.
12) Para fornecimento de proposta para execução da obra, a contratada responsável pela execução deverá considerar todos os elementos e componentes necessários para o pleno funcionamento do sistema, mesmo quando os itens não estiverem claramente explícitos.
13) Para cargas maiores do que as dimencionadas e/ou acréscimo de circuitos deverá ser verificado se os mesmos estão condizentes com a carga indicada como "reserva" nos quadros de carga e diagramas.
14) Nos trechos com circulação de veículos, o barramento blindado deverá possuir 2,30metros livres abaixo do barramento blindado. Conforme Manual Especial E-321.0003 BARRAMENTO BLINDADO (BUS-WAY).
15) Luminárias sujeitas a contato com a água devem ser alimentados em extrabaixa tensão, limitada a 12V-CA ou 30V-VCC.

LEGENDA	
	Eletroduto Embutido - sobe / desce / passa
	Eletroduto Aparente - sobe / desce / passa
	Aterramento - sobe / desce / passa
	Barramento Blindado - sobe / desce / passa
	Telemedição - sobe / desce / passa
	Automação Sinal - sobe / desce / passa
	Automação - sobe / desce / passa
	Eletrocalha - sobe / desce / passa

LISTA RESTRITA	01
PLANTA BAIXA	02
DIAGRAMA VERTICAL	03
DIAGRAMA VERTICAL	04
QUADRO ELÉTRICO	05
LISTA MEMORIAL	06